


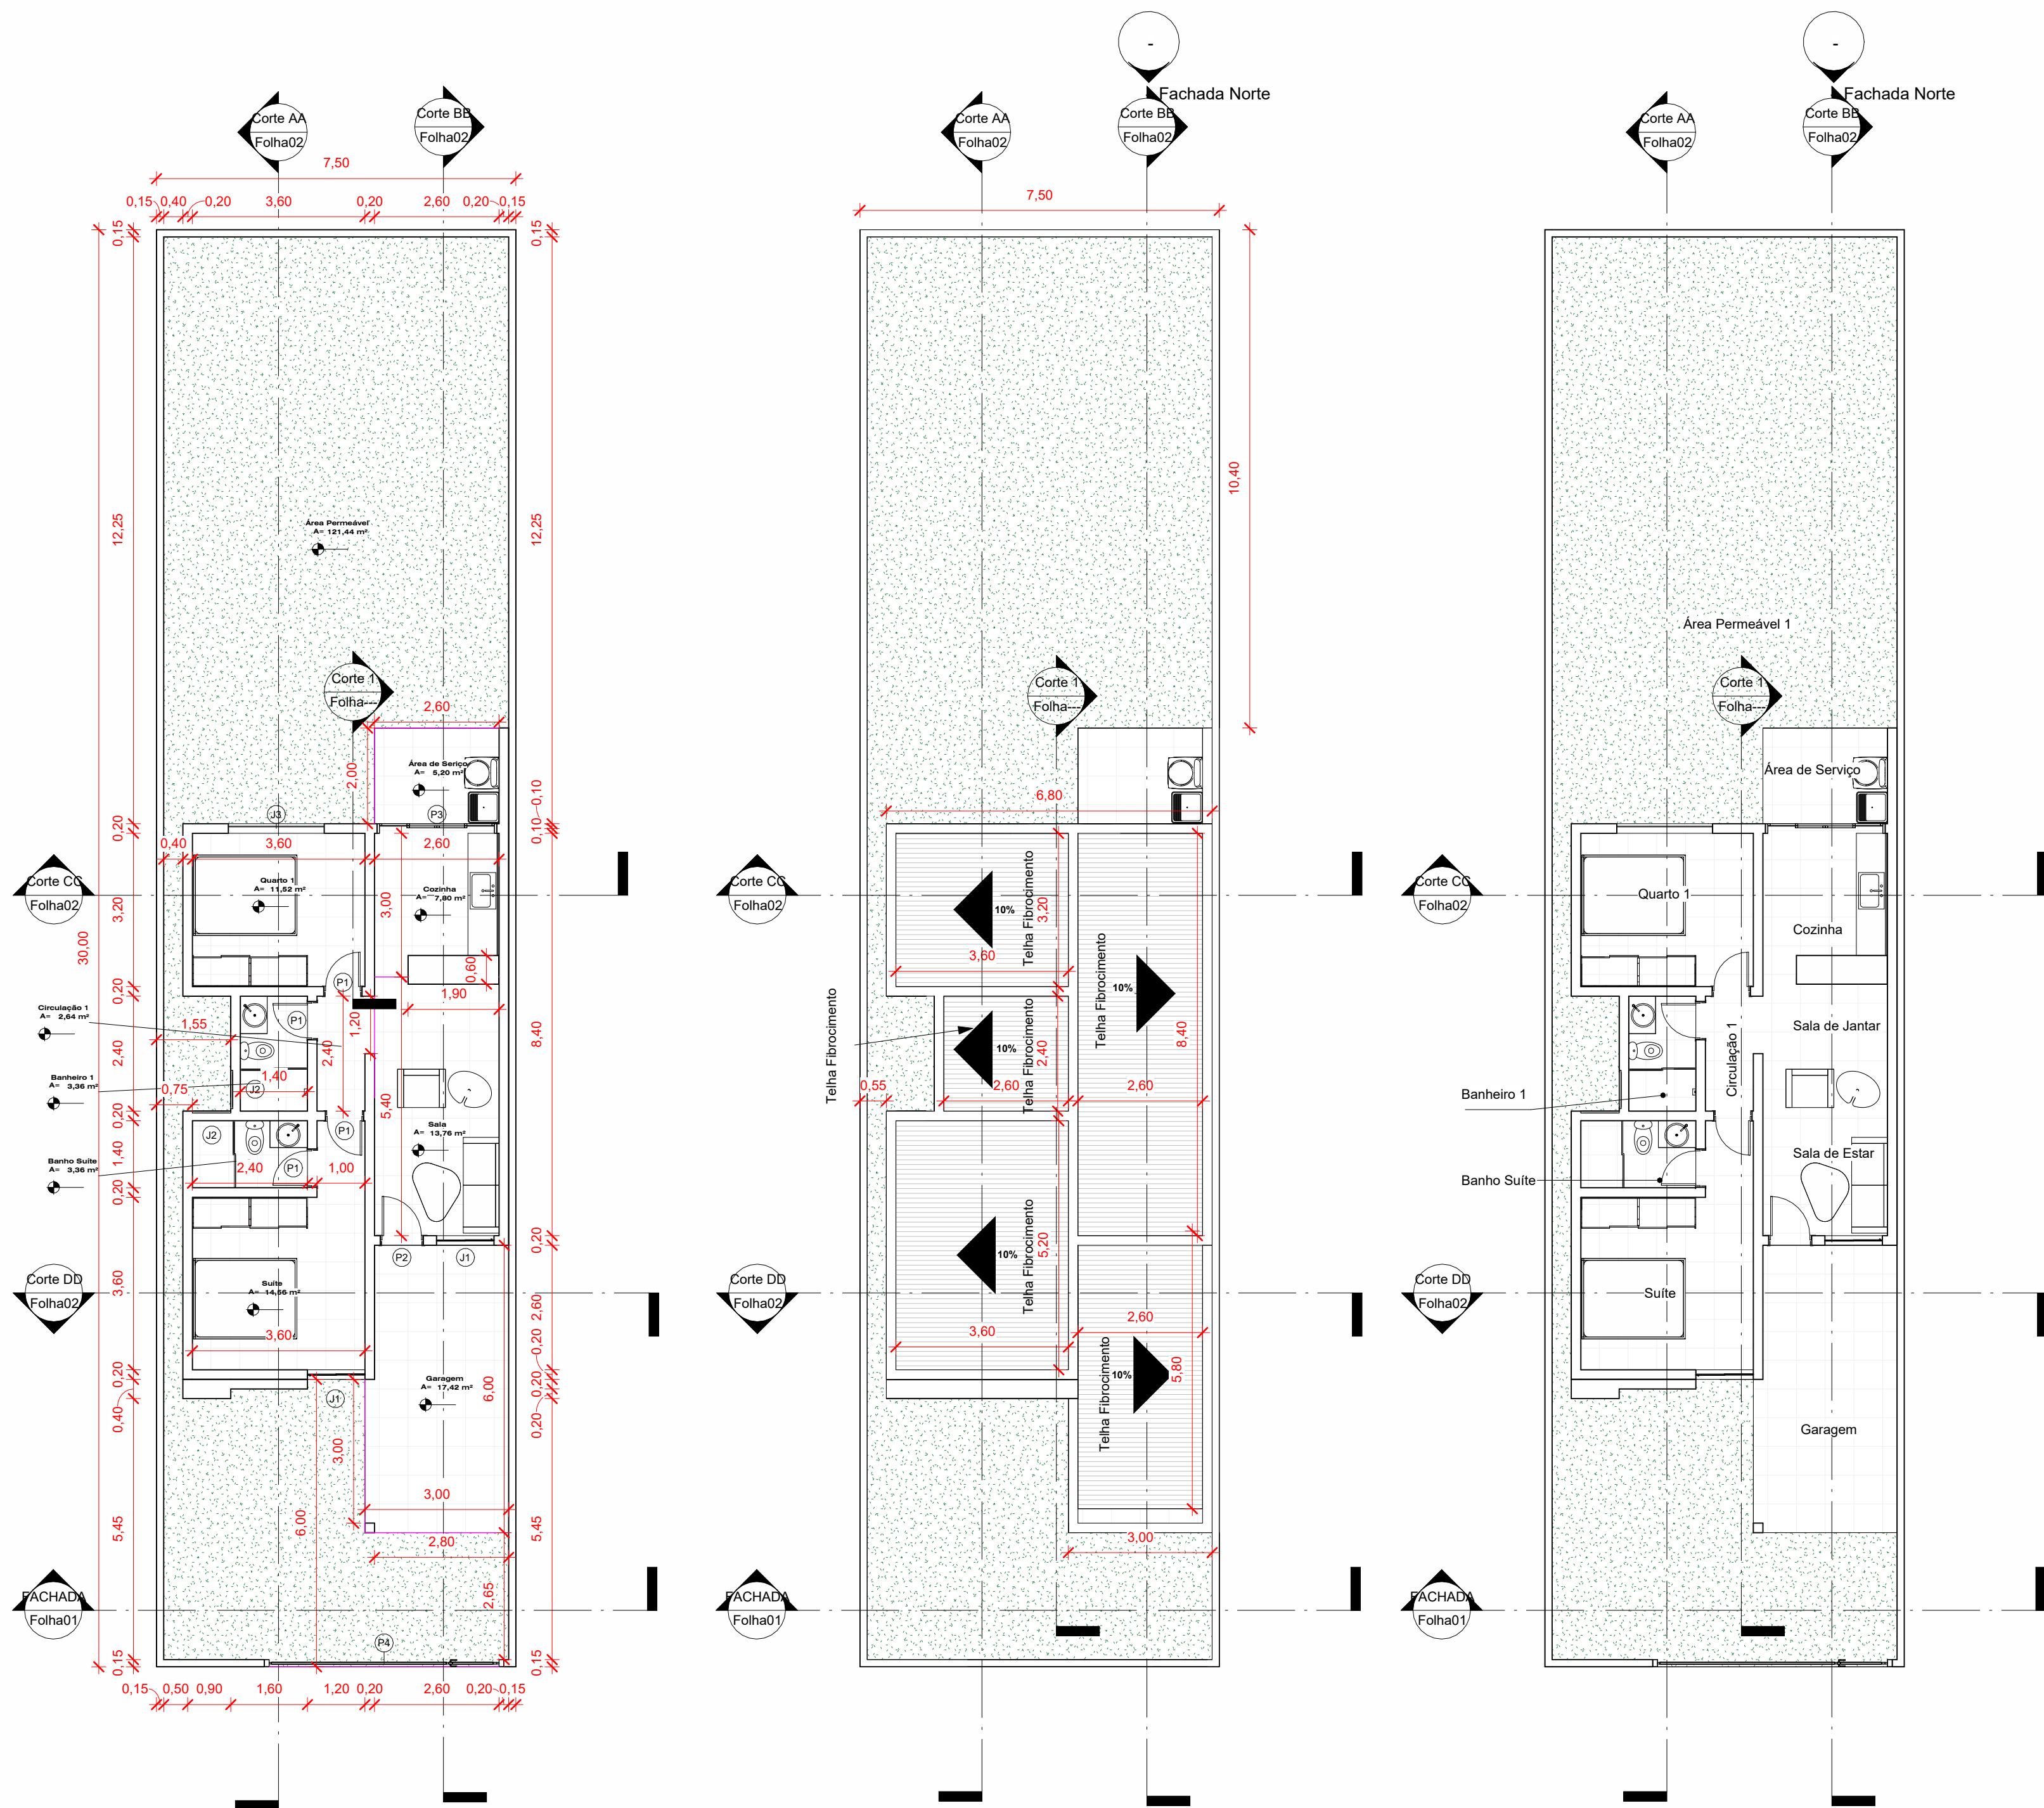

1 Planta Baixa -Térreo
1 : 100

2 Planta de Cobertura
1 : 100



3 Layout
1 : 100

4 Perspectiva


QUADRO DE ESQUADRIAS - JANELAS					
DENOMIN AÇÃO	LARGURA	ALTURA	ALTURA DO PEITORIL	TIPO	QUANTIDA DE
J1	1,20	1,20	1,00	Janela de correr 2 folhas - Alumínio e vidro	2
J2	0,80	0,60	1,80	Janela Maxim ar 1 folha - Alumínio e vidro	2
J3	2,00	1,00	1,10	Janela de correr 4 folhas - Alumínio e vidro	1

QUADRO DE ESQUADRIAS - PORTAS				
Marca de tipo	LARGURA	ALTURA	TIPO	QUANTIDA DE
P1	0,80	2,10	Porta Interior de Giro	4
P2	0,90	2,10	Porta Interior de Giro	1
P3	2,50	2,10	Porta de correr 4 folhas - Vidro	1
P4	5,00	2,10	Porta de correr em metal	1

5 FACHADA
1 : 100

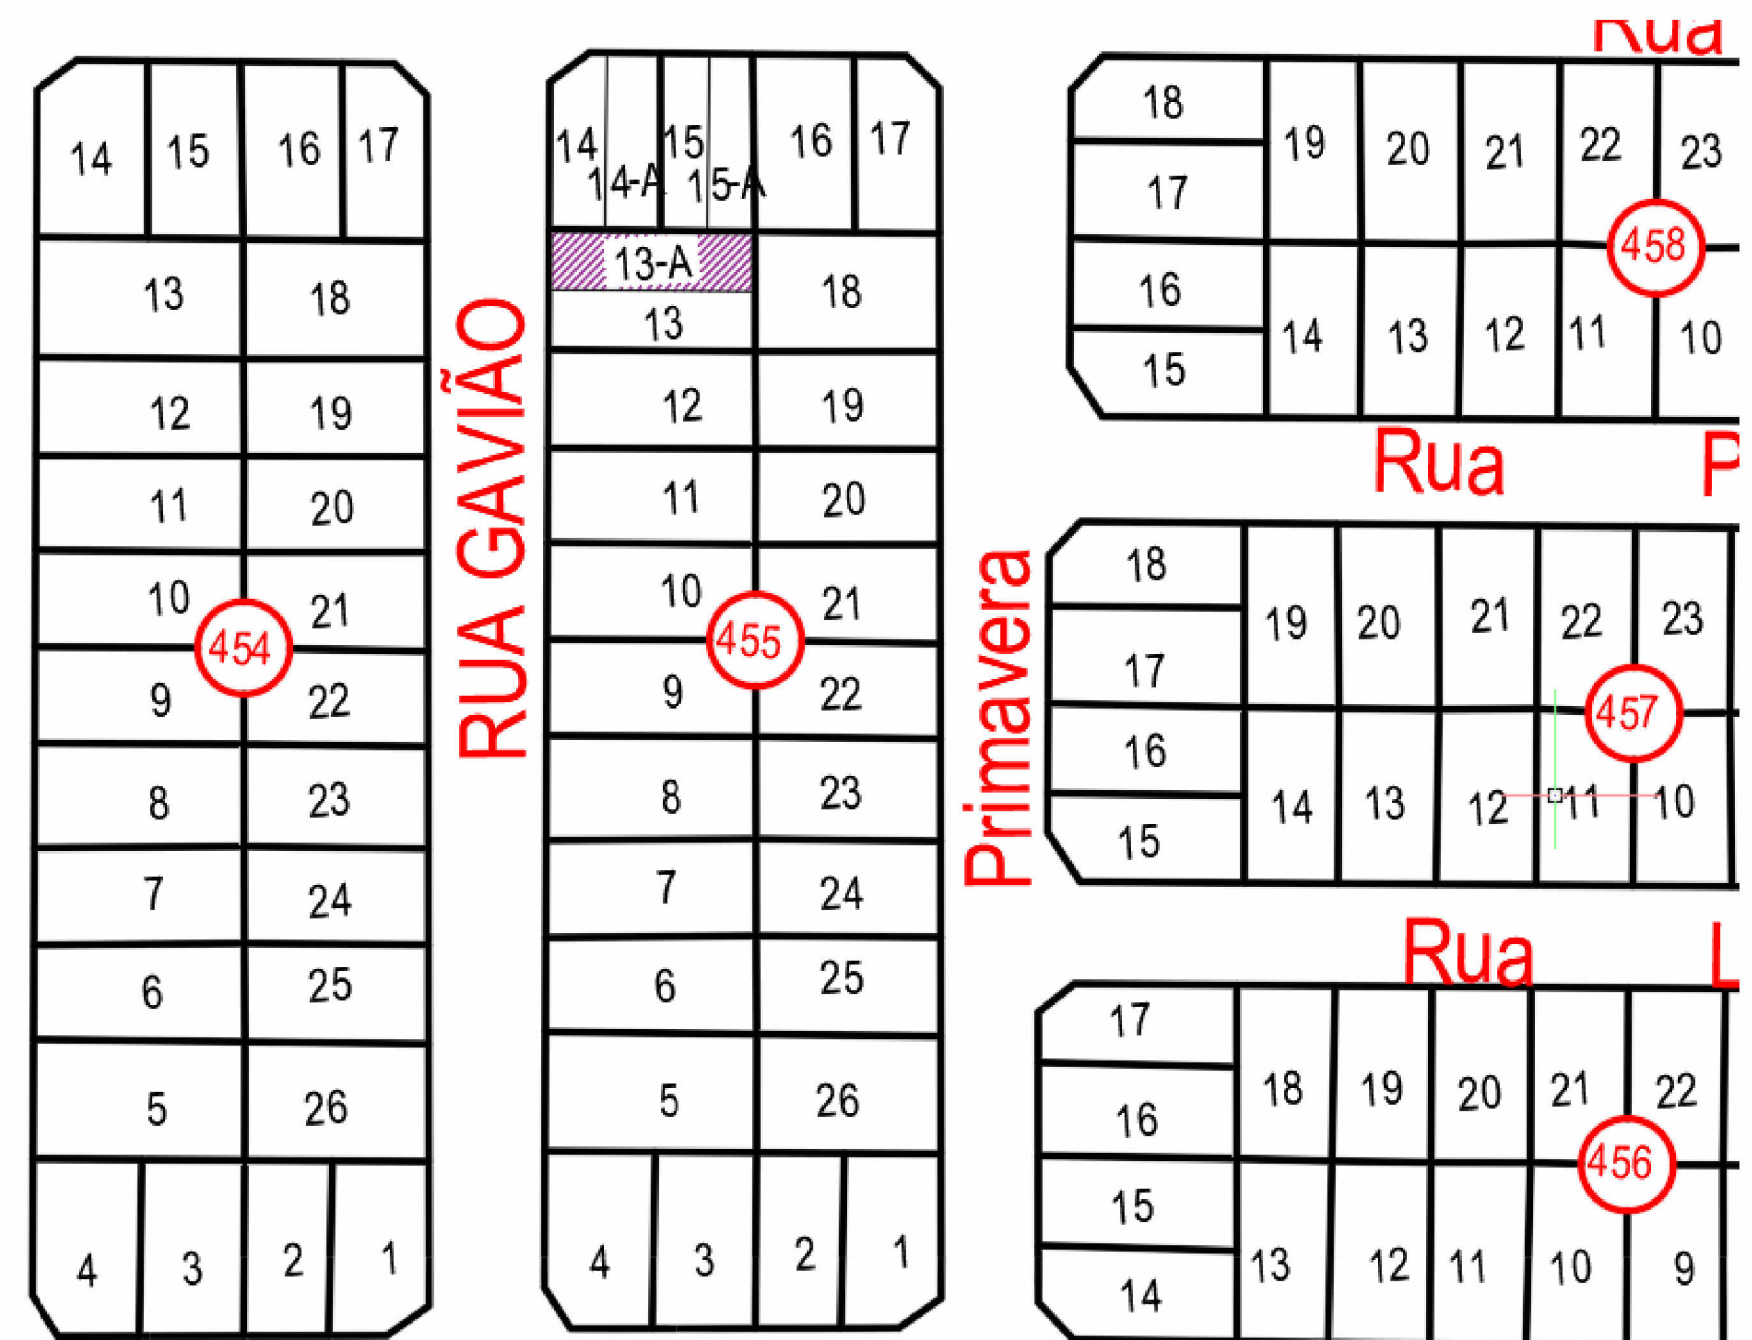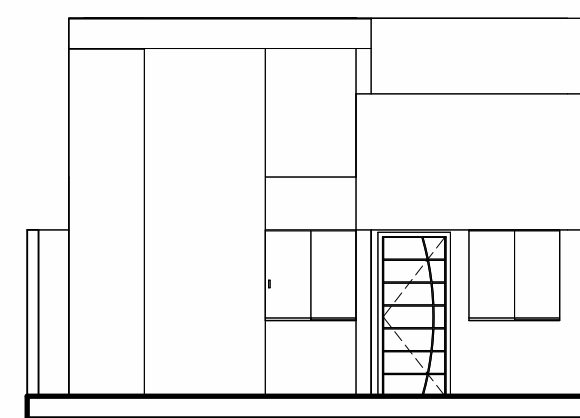

Planta de Situação

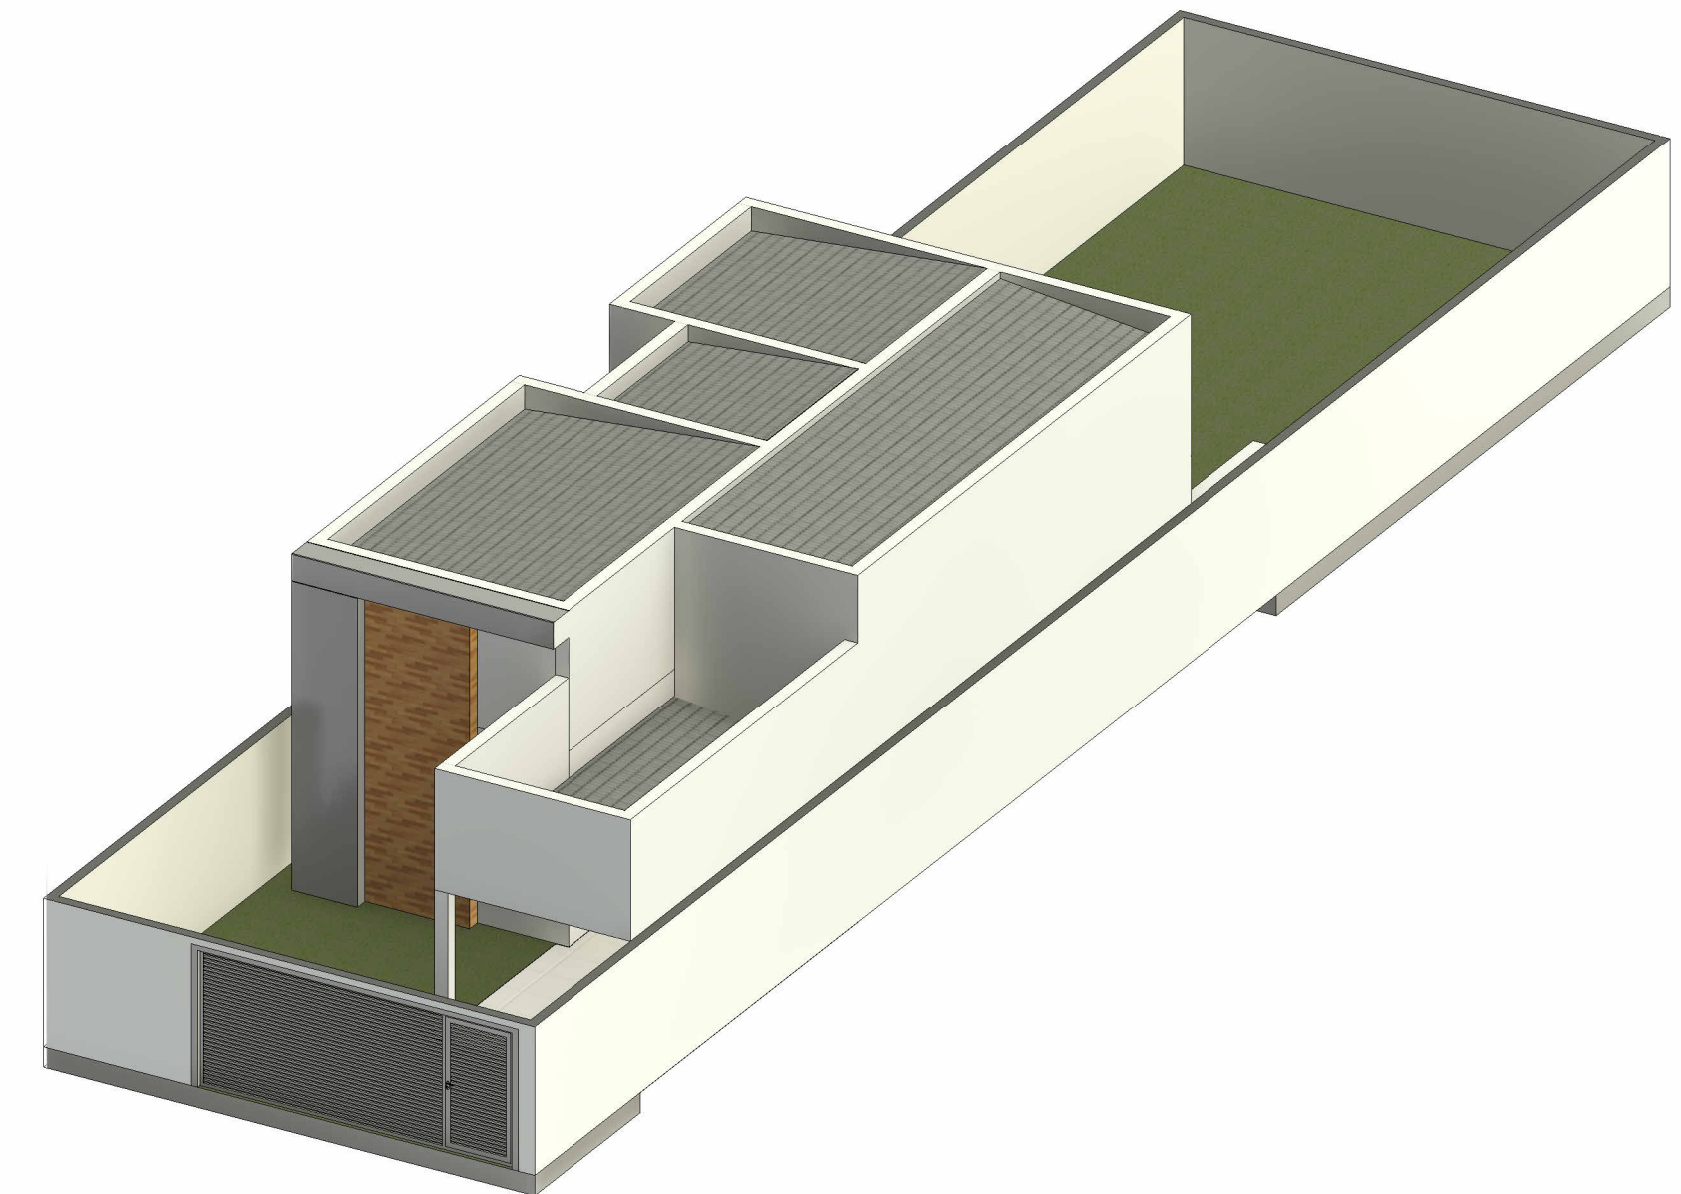

PROJETOS E OBRAS



www.leveengenharia.com - (66) 3401-2086 - contato@leveengenharia.com

PROJETO ARQUITETÔNICO

PROJETO RESIDENCIAL UNIFAMILIAR

Rua Gavião, Lote 13-A, Quadra 455, Jardim Nova Barra do Garças, Barra do

Garças, Mato Grosso

CONTEÚDO:

Planta Baixa do Térreo, Planta de Cobertura,

Planta de Situação, Layout, Perspectiva, Quadro

de Esquadrias, Fachada

ÁREAS:

Construída: 98,36m²

Passeio: 5,20m²

Permeável: 121,44m²

Lote: 225,00m²

DATA: ABRIL/2026

ESCALA: 1 : 100

Nº PRANCHA:

01/02

PROPRIETÁRIO: KAROLAYNE NAYARA ALVES


GOIS

CPF: 034.350.371-99


RESPONSÁVEL TÉCNICO: Eng. Vitor Hugo dos Santos

(CREA Nº: 1015135870)




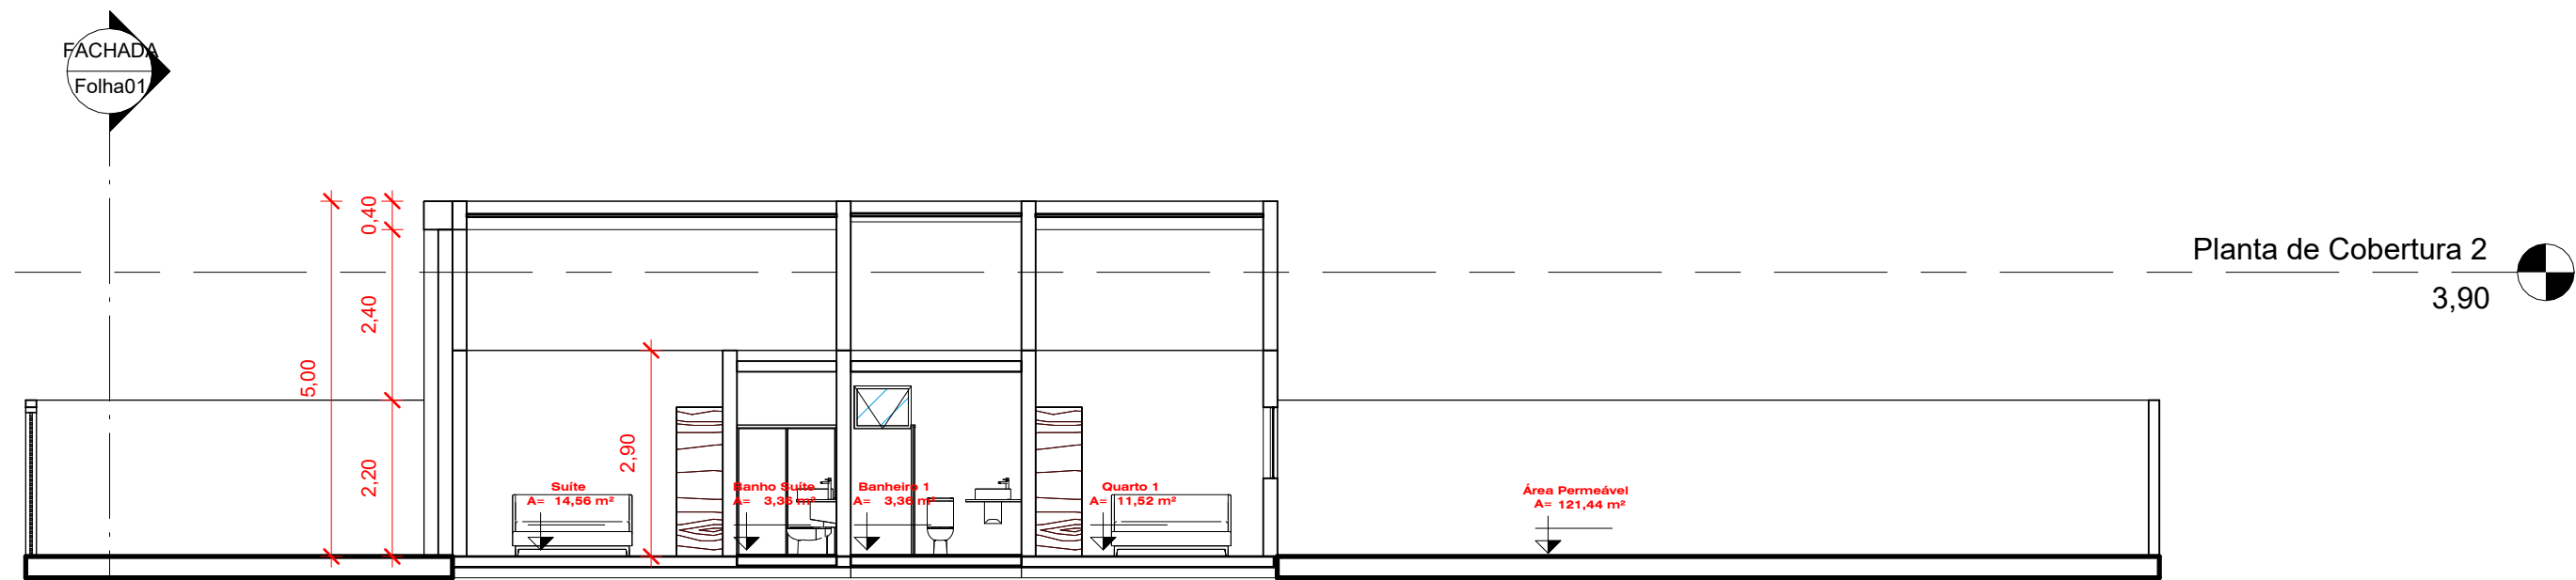


1 Corte AA
1 : 100

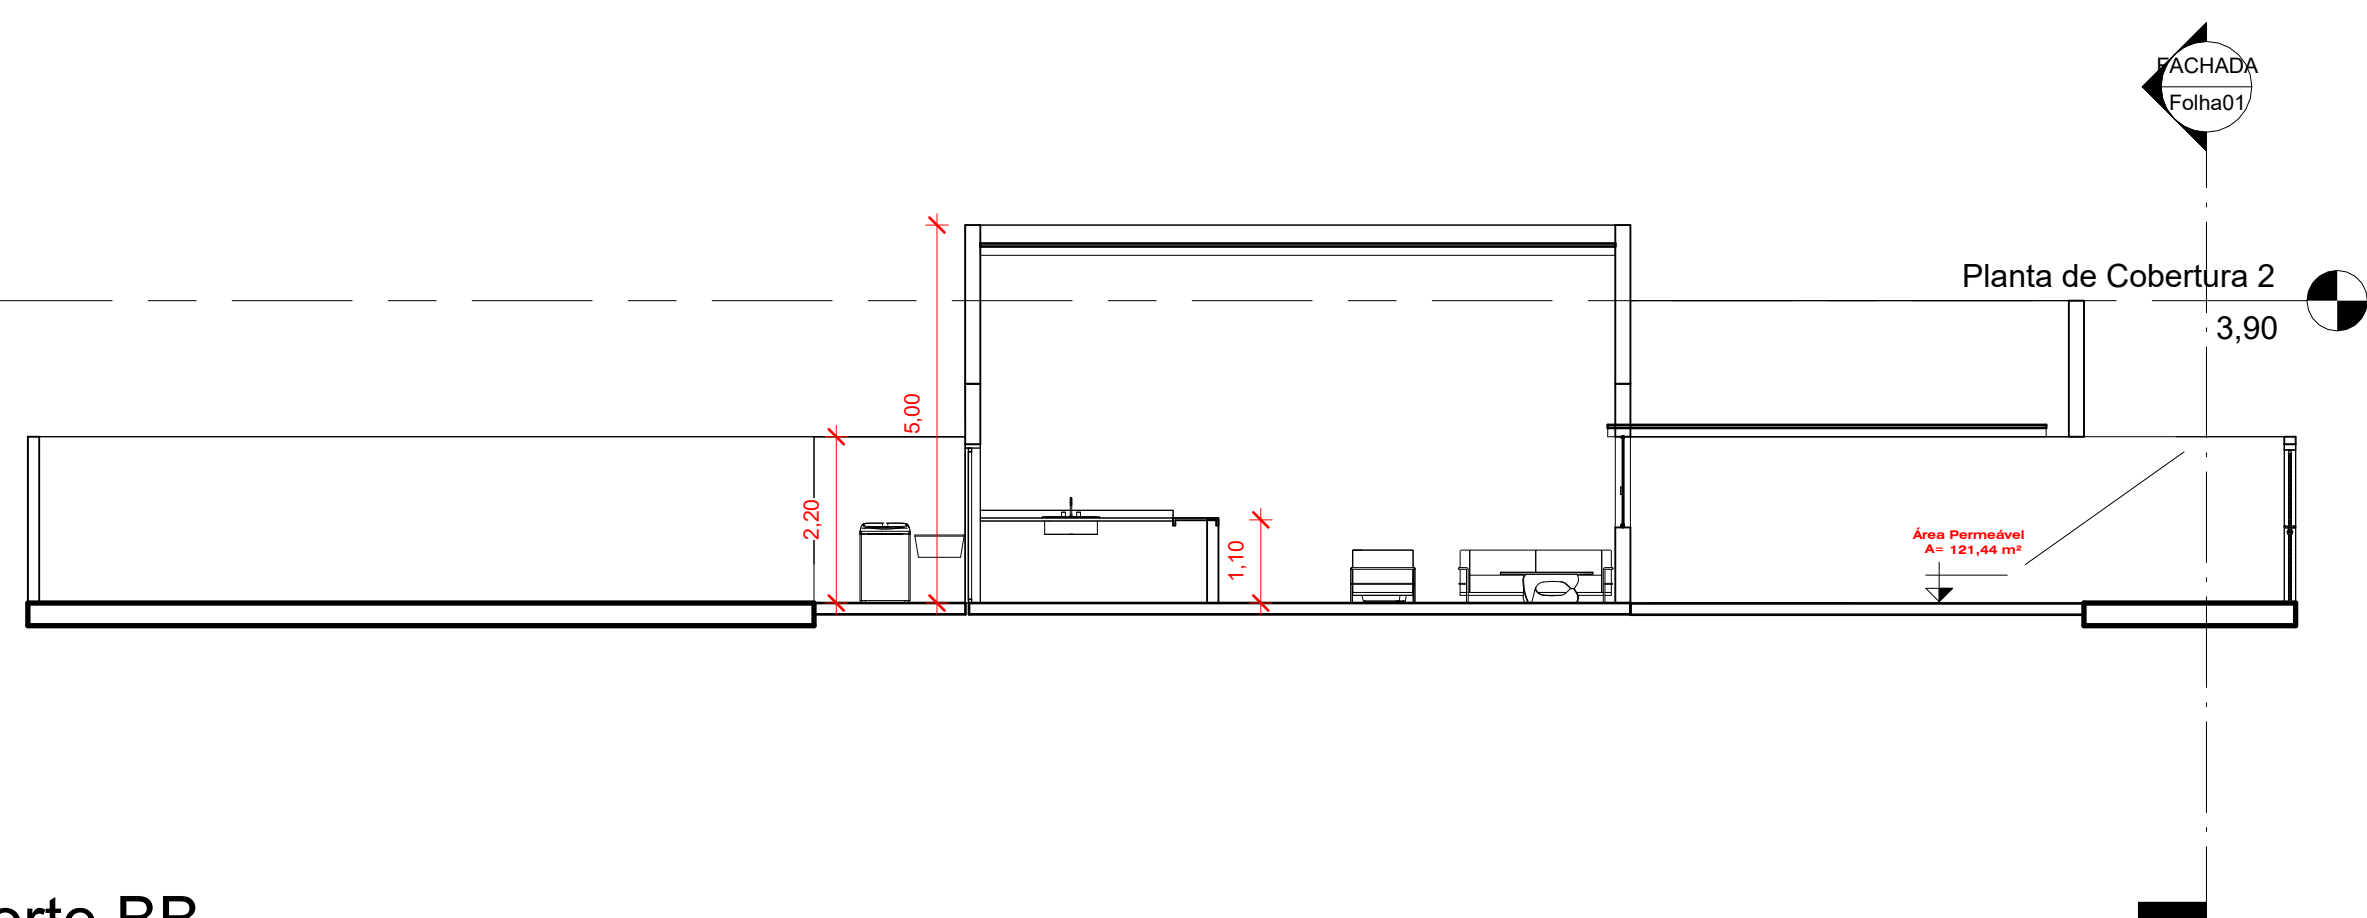

2 Corte BB
1 : 100

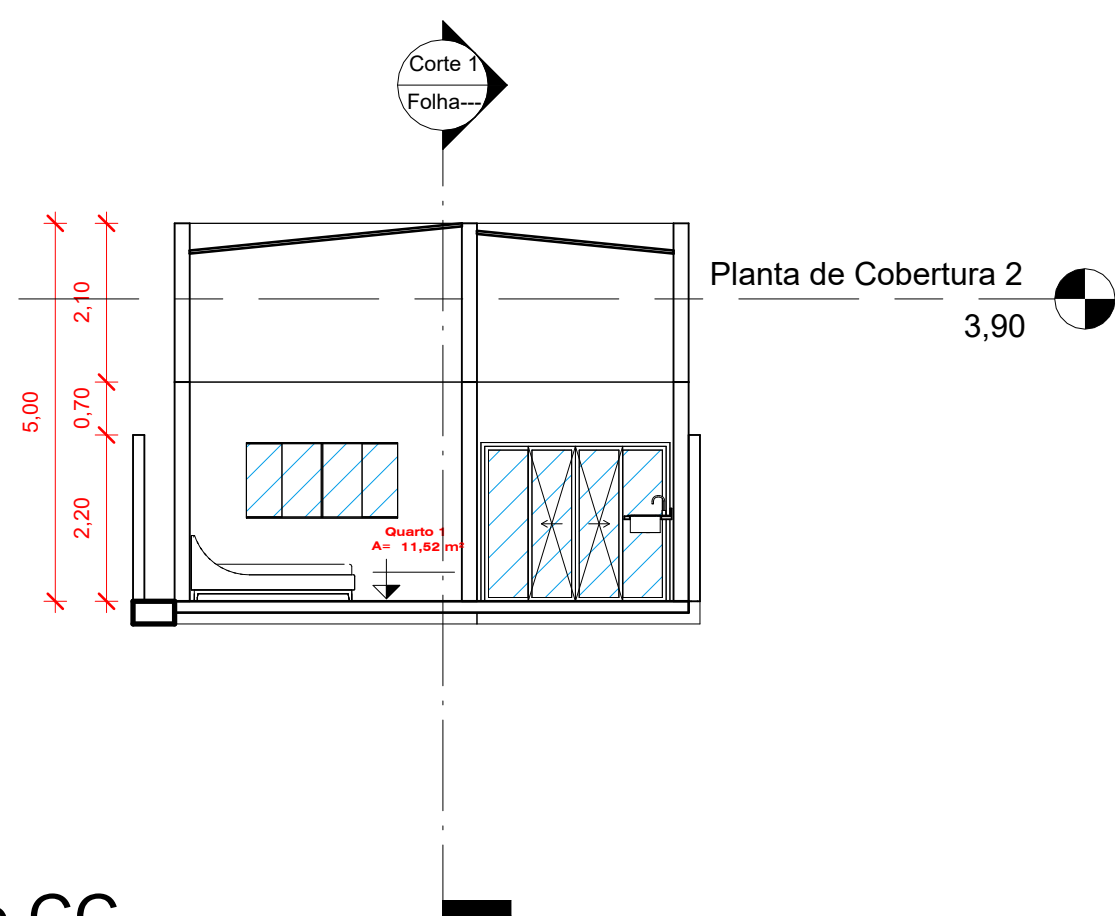

3 Corte CC
1 : 100

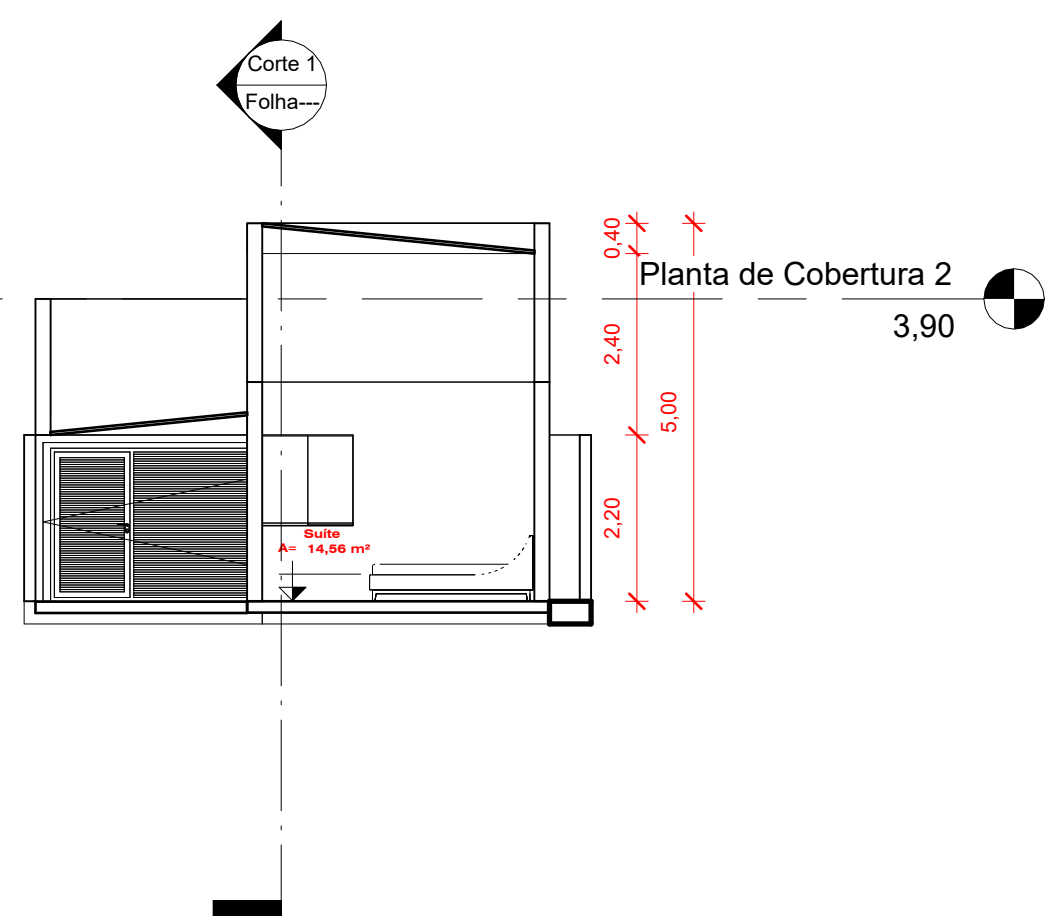

4 Corte DD
1 : 100

PROJETO ARQUITETÔNICO

PROJETO RESIDENCIAL UNIFAMILIAR

Rua Gavião, Lote 13-A, Quadra 455, Jardim Nova Barra do Garças, Barra do Garças, Mato Grosso

CONTEÚDO:
Cortes longitudinais AA e BB. Cortes transversais CC e DD.

ÁREAS:
Construída: 98,36m²
Passeio: 5,20m²
Permeável: 121,44m²
Lote: 225,00m²

Nº PRANCHA:
02/02

ESCALA:
1 : 100

PROPRIETÁRIO: KAROLAYNE NAYARA ALVES GOIS

CPF: 034.350.371-99

RESPONSÁVEL TÉCNICO: Eng. Vitor Hugo dos Santos
(CREA Nº: 1015135870)

